
ESTACIONAMIENTO PÚBLICO

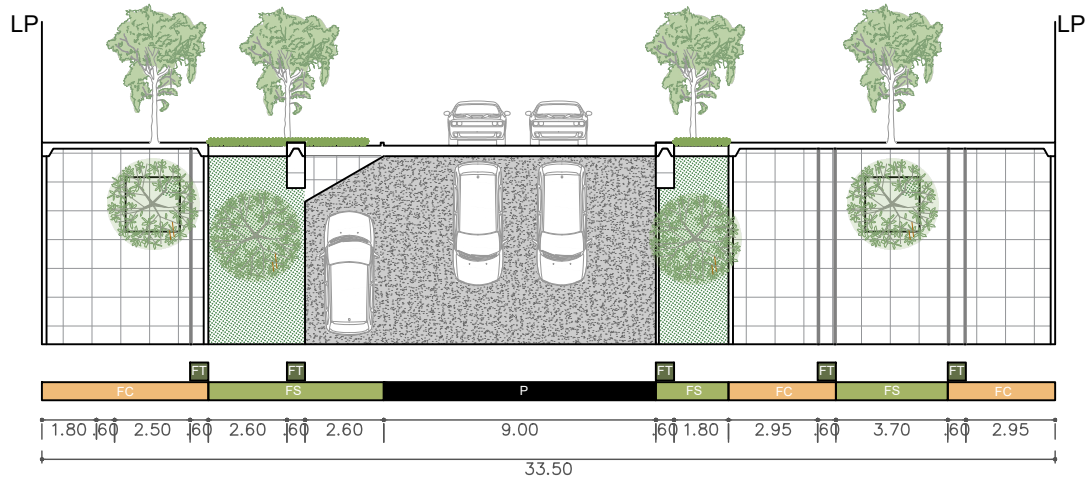

1. FS: Si es que no se cumple el ancho mínimo normativo para el estacionamiento del vehículo este no debe quedar expuesto en la pista PRINCIPAL (PP). De no existir zona rígida ni vegetación el ancho de la franja de servicio para estacionamiento será de 2.60m.
2. FS: Si la Franja de Servicio mide mayor o igual a 1.20m. se debe implementar arborización indicada en el Reglamento de Ornato y Mobiliario.
3. FT: En la Franja Técnica de pueden colocar postes de telefonía, postes de luz, señalética vertical, tachos segregadores y elementos similares indicados en el Reglamento de Ornato y Mobiliario.
4. FC: Si la Franja de Circulación mide mayor o igual a 1.80m. se debe incluir loseta podotáctil indicada en el Reglamento de Ornato y Mobiliario.

JIRÓN PAOLO UCCELLO (33.50 m)

Sector: 3

Subsector: A

Tramo: Jr. Vittore Scarpazza Carpaccio - Av. Javier Prado Este

NOTAS:


1. Cualquier elemento que se instale en la Franja Técnica deberá formar parte del Núcleo Técnico Urbano, entendido como el sistema que organiza y agrupa los elementos autorizados dentro del espacio público, a fin de evitar instalaciones aisladas que comprometan la continuidad, la legibilidad y la seguridad del recorrido peatonal.

NOTA SOBRE LA APLICACIÓN DE LAS FRANJAS FUNCIONALES Y LOS ESTACIONAMIENTOS PÚBLICOS EXISTENTES:
Cuando la implementación de las franjas funcionales implique la reducción o eliminación de estacionamientos públicos existentes, no serán exigibles estacionamientos suplementarios a los establecimientos comerciales con frente a esta vía, cuyos titulares hayan obtenido su licencia de funcionamiento con anterioridad a la entrada en vigencia de la normativa municipal que aprueba las franjas funcionales.

LEYENDA

LP = LÍMITE DE PROPIEDAD
V = VEREDA
J/E = JARDÍN / ESTACIONAMIENTO
VC = VÍA CICLISTA
BC = BERMA CENTRAL
PP = PISTA PRINCIPAL
PS = PISTA SECUNDARIA
FE = FRANJA EXCEPCIONAL
FS = FRANJA DE SERVICIO
FT = FRANJA TÉCNICA
FC = FRANJA DE CIRCULACIÓN
S = SEPARADOR CENTRAL O LATERAL
TP = PISTA EXCLUSIVA DE TRANSPORTE PÚBLICO COLECTIVO

ESPACIO PAISAJISTA

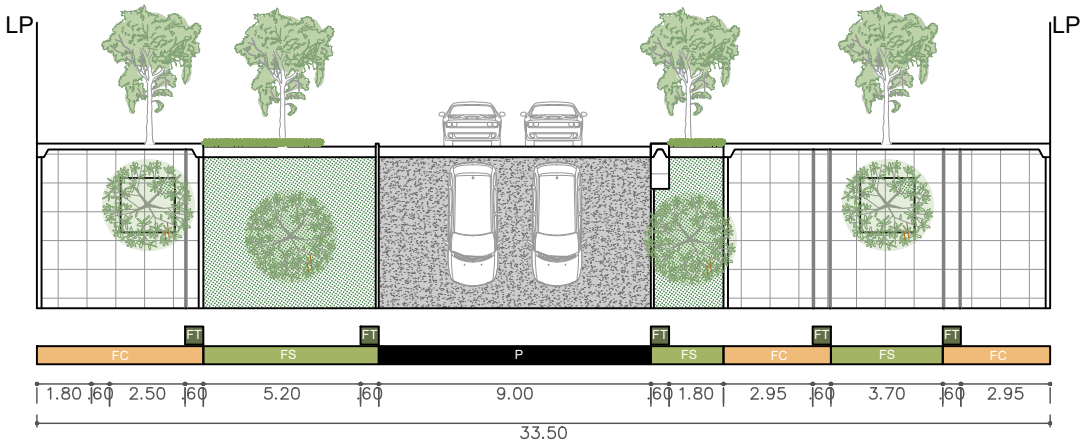

1. FS: Si la Franja de Servicio mide mayor o igual a 1.20m. se debe implementar arborización indicada en el Reglamento de Ornato y Mobiliario.
2. FT: En la Franja Técnica se pueden colocar postes de telefonía, postes de luz, señalética vertical, tachos segregadores y elementos similares indicados en el Reglamento de Ornato y Mobiliario.
3. FC: Si la Franja de Circulación mide mayor o igual a 1.80m. se debe incluir loseta podotáctil indicada en el Reglamento de Ornato y Mobiliario.

JIRÓN PAOLO UCCELLO (33.50 m)

Sector: 3

Subsector: A

Tramo: Jr. Vittore Scarpazza Carpaccio - Av. Javier Prado Este

NOTAS:

1. Cualquier elemento que se instale en la Franja Técnica deberá formar parte del Núcleo Técnico Urbano, entendido como el sistema que organiza y agrupa los elementos autorizados dentro del espacio público, a fin de evitar instalaciones aisladas que comprometan la continuidad, la legibilidad y la seguridad del recorrido peatonal.

NOTA SOBRE LA APLICACIÓN DE LAS FRANJAS FUNCIONALES Y LOS ESTACIONAMIENTOS PÚBLICOS EXISTENTES:
Cuando la implementación de las franjas funcionales implique la reducción o eliminación de estacionamientos públicos existentes, no serán exigibles estacionamientos suplementarios a los establecimientos comerciales con frente a esta vía, cuyos titulares hayan obtenido su licencia de funcionamiento con anterioridad a la entrada en vigencia de la normativa municipal que aprueba las franjas funcionales.

LEYENDA

LP = LÍMITE DE PROPIEDAD
V = VEREDA
J/E = JARDÍN / ESTACIONAMIENTO
VC = VÍA CICLISTA
BC = BERMA CENTRAL
PP = PISTA PRINCIPAL
PS = PISTA SECUNDARIA
FE = FRANJA EXCEPCIONAL
FS = FRANJA DE SERVICIO
FT = FRANJA TÉCNICA
FC = FRANJA DE CIRCULACIÓN
S = SEPARADOR CENTRAL O LATERAL
TP = PISTA EXCLUSIVA DE TRANSPORTE PÚBLICO COLECTIVO

MUNICIPALIDAD DE SAN BORJA

ANEXO 01 DEL REGLAMENTO DE GESTIÓN DE ESPACIOS PÚBLICOS: FRANJAS FUNCIONALES DEL SISTEMA VIAL DEL DISTRITO DE SAN BORJA

Descripción: SISTEMA VIAL DISTRITAL DE SAN BORJA

Vía: JIRÓN PAOLO UCCELLO

Escala: 1/250

Distrito: SAN BORJA

Año: 2026

Lámina: VLP-JR-56B (2 de 2)