


ESPACIO PAISAJISTA

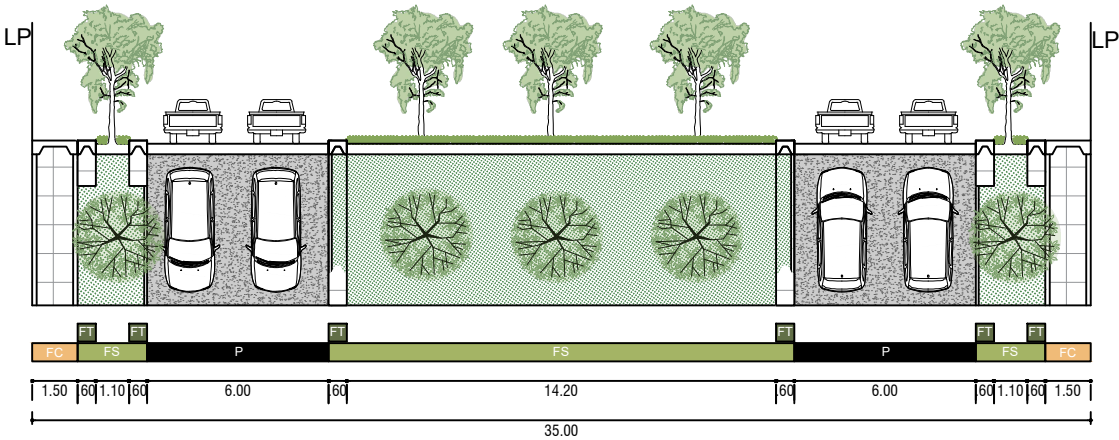

1. FS: Si la Franja de Servicio mide mayor o igual a 1.20 m, se debe implementar arborización indicada en el Reglamento de Ornato y Mobiliario.
2. FT: En la Franja Técnica se pueden colocar postes de telefonía, postes de luz, señalética vertical, tachos segregadores y elementos similares indicados en el Reglamento de Ornato y Mobiliario.
3. FC: Si la Franja de Circulación mide mayor o igual a 1.80 m, se debe incluir loseta podotáctil indicada en el Reglamento de Ornato y Mobiliario.

AVENIDA ESMERALDA (35 m)

Sector: 12
Subsector: B
Tramo: Jr. Galeon - Av. Tnte. Alejandro Velasco Astete

NOTAS:
1. Cualquier elemento que se instale en la Franja Técnica deberá formar parte del Núcleo Técnico Urbano, entendido como el sistema que organiza y agrupa los elementos autorizados dentro del espacio público, a fin de evitar instalaciones aisladas que comprometan la continuidad, la legibilidad y la seguridad del recorrido peatonal.

LEYENDA

- | | |
|--------------------------------|--|
| LP = LÍMITE DE PROPIEDAD | |
| V = VEREDA | FE = FRANJA EXCEPCIONAL |
| J/E = JARDÍN / ESTACIONAMIENTO | FS = FRANJA DE SERVICIO |
| VC = VÍA CICLISTA | FT = FRANJA TÉCNICA |
| BC = BERMA CENTRAL | FC = FRANJA DE CIRCULACIÓN |
| PP = PISTA PRINCIPAL | S = SEPARADOR CENTRAL O LATERAL |
| PS = PISTA SECUNDARIA | TP = PISTA EXCLUSIVA DE TRANSPORTE PÚBLICO COLECTIVO |



ANEXO 01 DEL REGLAMENTO DE ESPACIOS PÚBLICOS:
FRANJAS FUNCIONALES DEL SISTEMA VIAL DEL
DISTRITO DE SAN BORJA

Descripción: SISTEMA VIAL DISTRITAL DE SAN BORJA

Vía: AVENIDA ESMERALDA

Escala:
1/250

Distrito:
SAN BORJA

Año:
2026

Lámina:

VLP-AV-10B