


ESPACIO PAISAJISTA

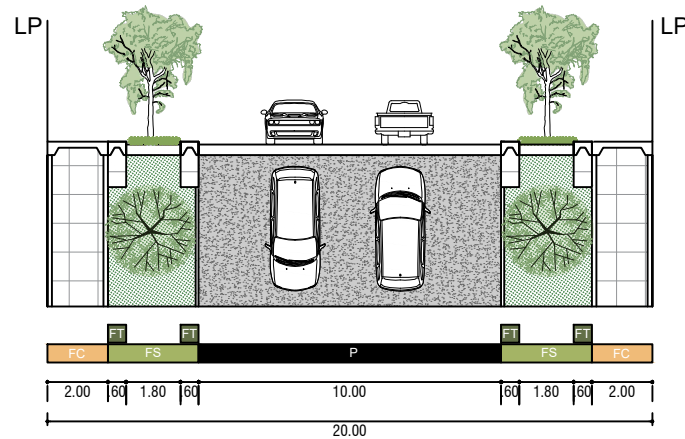

1. FS: Si la Franja de Servicio mide mayor o igual a 1.20m; se debe implementar arborización indicada en el Reglamento de Ornato y Mobiliario.
2. FT: En la Franja Técnica se pueden colocar postes de telefonía, postes de luz, señalética vertical, tachos segregadores y elementos similares indicados en el Reglamento de Ornato y Mobiliario.
3. FC: Si la Franja de Circulación mide mayor o igual a 1.80m; se deberá incluir loseta podotáctil, de acuerdo con lo indicado en el Reglamento de Ornato y Mobiliario.

CALLE DE LA PROSA (20 m)

Sector: 1

Subsector: A

Tramo: Av. De La Poesia - Av. Del Aire

NOTAS:

1. Cualquier elemento que se instale en la Franja Técnica deberá formar parte del Núcleo Técnico Urbano, entendido como el sistema que organiza y agrupa los elementos autorizados dentro del espacio público, a fin de evitar instalaciones aisladas que comprometan la continuidad, la legibilidad y la seguridad del recorrido peatonal.

LEYENDA

LP = LÍMITE DE PROPIEDAD

V = VEREDA

J/E = JARDÍN / ESTACIONAMIENTO

VC = VÍA CICLISTA

BC = BERMA CENTRAL

PP = PISTA PRINCIPAL

PS = PISTA SECUNDARIA

FE = FRANJA EXCEPCIONAL

FS = FRANJA DE SERVICIO

FT = FRANJA TÉCNICA

FC = FRANJA DE CIRCULACIÓN

S = SEPARADOR CENTRAL O LATERAL

TP = PISTA EXCLUSIVA DE TRANSPORTE PÚBLICO COLECTIVO



ANEXO 01 DEL REGLAMENTO DE ESPACIOS PÚBLICOS:
FRANJAS FUNCIONALES DEL SISTEMA VIAL DEL
DISTRITO DE SAN BORJA

Descripción: SISTEMA VIAL DISTRITAL DE SAN BORJA

Vía: CALLE DE LA PROSA

Escala:
1/250

Distrito:
SAN BORJA

Año:
2026

Lámina:

VLP-CA-17