


ESPACIO PAISAJISTA

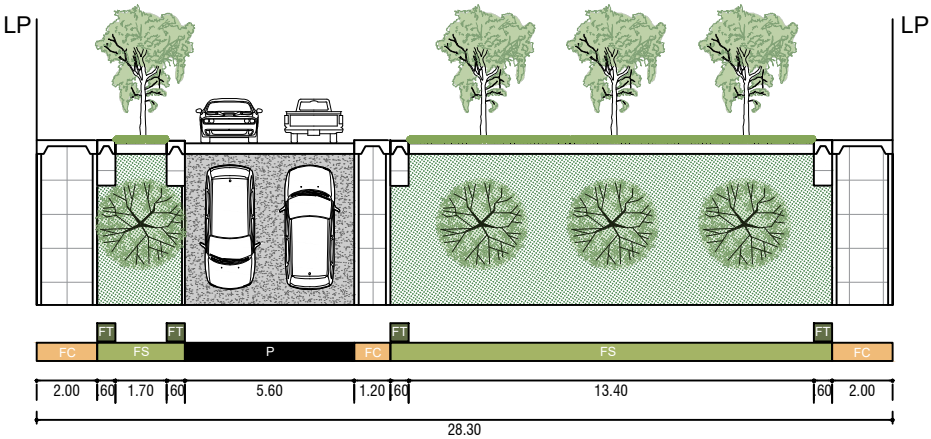

- 1. FS: Si la Franja de Servicio mide mayor o igual a 1.20m; se debe implementar arborización indicada en el Reglamento de Ornato y Mobiliario.
- 2. FT: En la Franja Técnica se pueden colocar postes de telefonía, postes de luz, señalética vertical, tachos segregadores y elementos similares indicados en el Reglamento de Ornato y Mobiliario.
- 3. FC: Si la Franja de Circulación mide mayor o igual a 1.80m; se deberá incluir loseta podotáctil, de acuerdo con lo indicado en el Reglamento de Ornato y Mobiliario.

CALLE DE LAS LETRAS (28.30 m)

Sector: 1
Subsector: A
Tramo: Av. Del Aire - Av. Luis Aldana

NOTAS:
1. Cualquier elemento que se instale en la Franja Técnica deberá formar parte del Núcleo Técnico Urbano, entendido como el sistema que organiza y agrupa los elementos autorizados dentro del espacio público, a fin de evitar instalaciones aisladas que comprometan la continuidad, la legibilidad y la seguridad del recorrido peatonal.

LEYENDA

LP = LÍMITE DE PROPIEDAD	
V = VEREDA	FE = FRANJA EXCEPCIONAL
J/E = JARDÍN / ESTACIONAMIENTO	FS = FRANJA DE SERVICIO
VC = VÍA CICLISTA	FT = FRANJA TÉCNICA
BC = BERMA CENTRAL	FC = FRANJA DE CIRCULACIÓN
PP = PISTA PRINCIPAL	S = SEPARADOR CENTRAL O LATERAL
PS = PISTA SECUNDARIA	TP = PISTA EXCLUSIVA DE TRANSPORTE PÚBLICO COLECTIVO



ANEXO 01 DEL REGLAMENTO DE ESPACIOS PÚBLICOS:
FRANJAS FUNCIONALES DEL SISTEMA VIAL DEL
DISTRITO DE SAN BORJA

Descripción: SISTEMA VIAL DISTRITAL DE SAN BORJA

Vía: CALLE DE LAS LETRAS

Escala:
1/250

Distrito:
SAN BORJA

Año:
2026

Lámina:

VLP-CA-20C