


ESPACIO PAISAJISTA

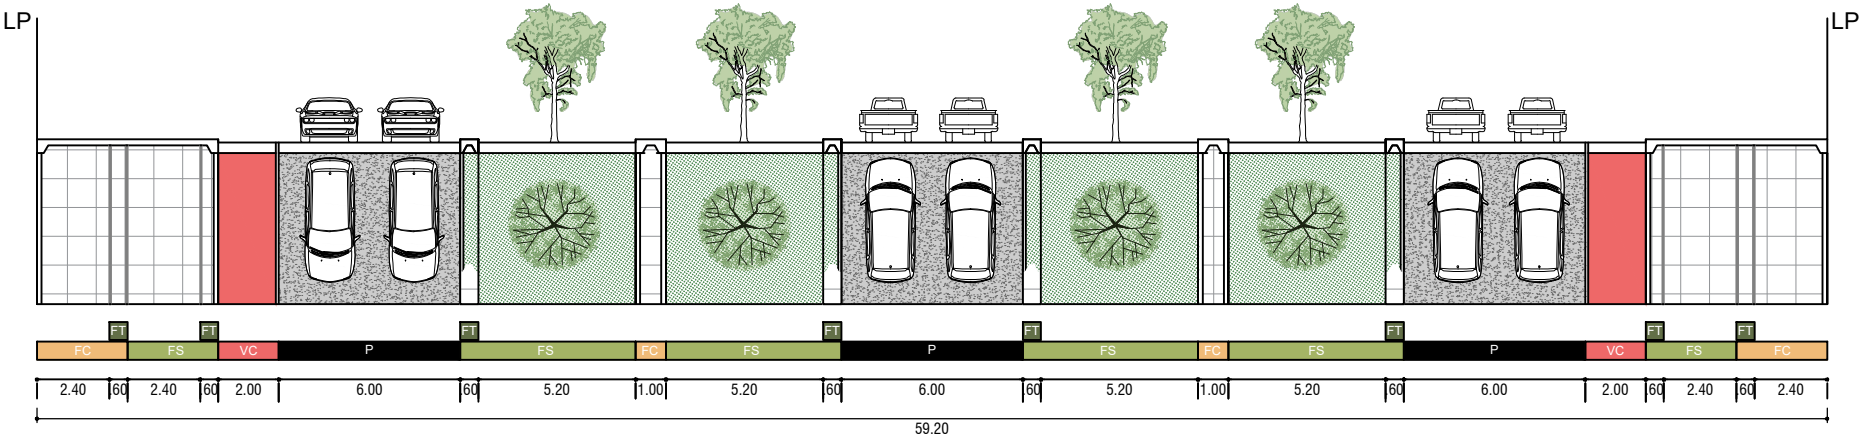

- 1. FS: Si la Franja de Servicio mide mayor o igual a 1.20m. se debe implementar arborización indicada en el Reglamento de Ornato y Mobiliario.
- 2. FT: En la Franja Técnica se pueden colocar postes de telefonía, postes de luz, señalética vertical, tachos segregadores y elementos similares indicados en el Reglamento de Ornato y Mobiliario.
- 3. FC: Si la Franja de Circulación mide mayor o igual a 1.80m. se debe incluir loseta podotáctil indicada en el Reglamento de Ornato y Mobiliario.

JIRÓN FREDERIC REMINGTON (59.20 m)

Sector: 6

Subsector: A

Tramo: Av. Del Parque Norte - Jr. Pietro Torrigiano

NOTAS:

- 1. Cualquier elemento que se instale en la Franja Técnica deberá formar parte del Núcleo Técnico Urbano, entendido como el sistema que organiza y agrupa los elementos autorizados dentro del espacio público, a fin de evitar instalaciones aisladas que comprometan la continuidad, la legibilidad y la seguridad del recorrido peatonal.

LEYENDA

LP = LÍMITE DE PROPIEDAD	FE = FRANJA EXCEPCIONAL
V = VEREDA	FS = FRANJA DE SERVICIO
J/E = JARDÍN / ESTACIONAMIENTO	FT = FRANJA TÉCNICA
VC = VÍA CICLISTA	FC = FRANJA DE CIRCULACIÓN
BC = BERMA CENTRAL	S = SEPARADOR CENTRAL O LATERAL
PP = PISTA PRINCIPAL	TP = PISTA EXCLUSIVA DE TRANSPORTE PÚBLICO COLECTIVO
PS = PISTA SECUNDARIA	



ANEXO 01 DEL REGLAMENTO DE ESPACIOS PÚBLICOS:
FRANJAS FUNCIONALES DEL SISTEMA VIAL DEL
DISTRITO DE SAN BORJA

Descripción: SISTEMA VIAL DISTRITAL DE SAN BORJA

Vía: JIRÓN FREDERIC REMINGTON

Escala:
1/250


Distrito:
SAN BORJA

Año:
2026

Lámina:

VLP-JR-29B
(1 de 2)

ESTACIONAMIENTO PÚBLICO

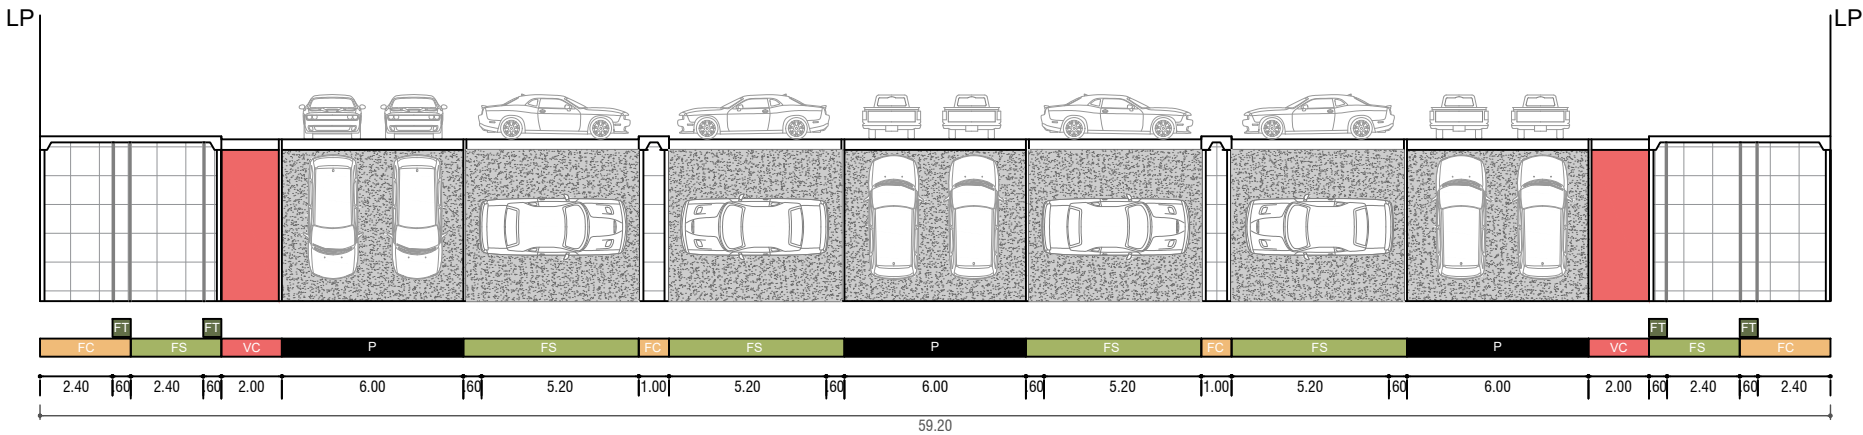

1. FS: Si es que no se cumple el ancho mínimo normativo para el estacionamiento del vehículo este no debe quedar expuesto en la pista PRINCIPAL (PP). De no existir zona rígida ni vegetación el ancho de la franja de servicio para estacionamiento será de 2.60m.
2. FS: Si la Franja de Servicio mide mayor o igual a 1.20m. se debe implementar arborización indicada en el Reglamento de Ornato y Mobiliario.
3. FT: En la Franja Técnica de pueden colocar postes de telefonía, postes de luz, señalética vertical, tachos segregadores y elementos similares indicados en el Reglamento de Ornato y Mobiliario.
4. FC: Si la Franja de Circulación mide mayor o igual a 1.80m. se debe incluir loseta podotáctil indicada en el Reglamento de Ornato y Mobiliario.

JIRÓN FREDERIC REMINGTON (59.20 m)

Sector: 6

Subsector: A

Tramo: Av. Del Parque Norte - Jr. Pietro Torrigiano

NOTAS:

1. Cualquier elemento que se instale en la Franja Técnica deberá formar parte del Núcleo Técnico Urbano, entendido como el sistema que organiza y agrupa los elementos autorizados dentro del espacio público, a fin de evitar instalaciones aisladas que comprometan la continuidad, la legibilidad y la seguridad del recorrido peatonal.

LEYENDA

- LP = LÍMITE DE PROPIEDAD
V = VEREDA
J/E = JARDÍN / ESTACIONAMIENTO
VC = VÍA CICLISTA
BC = BERMA CENTRAL
PP = PISTA PRINCIPAL
PS = PISTA SECUNDARIA
- FE = FRANJA EXCEPCIONAL
FS = FRANJA DE SERVICIO
FT = FRANJA TÉCNICA
FC = FRANJA DE CIRCULACIÓN
S = SEPARADOR CENTRAL O LATERAL
TP = PISTA EXCLUSIVA DE TRANSPORTE PÚBLICO COLECTIVO



ANEXO 01 DEL REGLAMENTO DE ESPACIOS PÚBLICOS:
FRANJAS FUNCIONALES DEL SISTEMA VIAL DEL
DISTRITO DE SAN BORJA

Descripción: SISTEMA VIAL DISTRITAL DE SAN BORJA

Vía: JIRÓN FREDERIC REMINGTON

Escala: 1/250

Distrito: SAN BORJA

Año: 2026

Lámina:

VLP-JR-29B
(2 de 2)