



ESPACIO PAISAJISTA

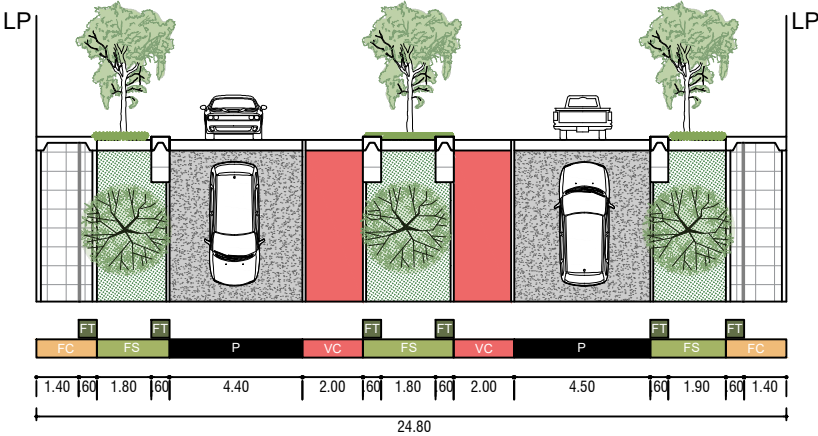

- 1. FS: Si la Franja de Servicio mide mayor o igual a 1.20 m, se debe implementar arborización indicada en el Reglamento de Ornato y Mobiliario.
- 2. FT: En la Franja Técnica se pueden colocar postes de telefonía, postes de luz, señalética vertical, tachos segregadores y elementos similares indicados en el Reglamento de Ornato y Mobiliario.
- 3. FC: Si la Franja de Circulación mide mayor o igual a 1.80 m, se debe incluir loseta podotáctil indicada en el Reglamento de Ornato y Mobiliario.

EXTENSIÓN DE COMERCIO

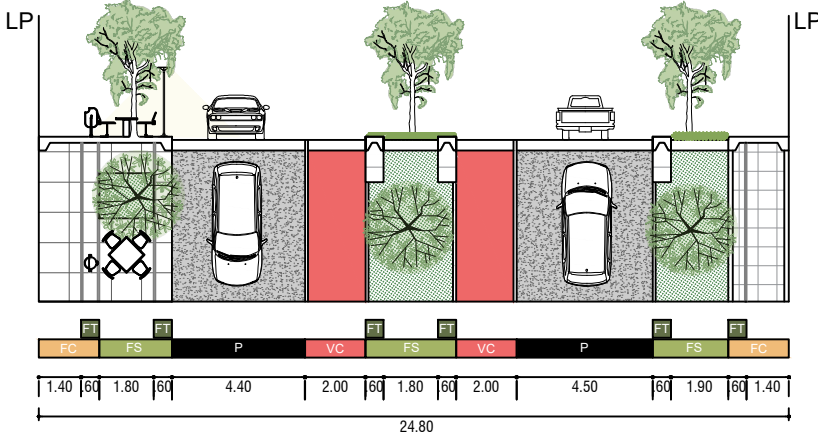

- 1. FC: Si la Franja de Circulación fuera colindante a un predio con licencia de funcionamiento se habilitará una extensión en la Franja de Servicio si es mayor o igual a 1.80 m, donde se debe implementar mobiliario que genere espacios de extensión para los comercios indicado en el Reglamento de Ornato y Mobiliario.
- 2. FT: En la Franja Técnica se pueden colocar postes de telefonía, postes de luz, señalética vertical, tachos segregadores y elementos similares indicados en el Reglamento de Ornato y Mobiliario.
- 3. FC: Si la Franja de Circulación mide mayor o igual a 1.80 m, se debe incluir loseta podotáctil indicada en el Reglamento de Ornato y Mobiliario.

AVENIDA DE LA POESIA (24.80 m)

Sector: 1

Subsector: A

Tramo: Av. Javier Prado Este - Av. Canada

NOTAS:

- 1. Cualquier elemento que se instale en la Franja Técnica deberá formar parte del Núcleo Técnico Urbano, entendido como el sistema que organiza y agrupa los elementos autorizados dentro del espacio público, a fin de evitar instalaciones aisladas que comprometan la continuidad, la legibilidad y la seguridad del recorrido peatonal.

LEYENDA

LP = LÍMITE DE PROPIEDAD	FE = FRANJA EXCEPCIONAL
V = VEREDA	FS = FRANJA DE SERVICIO
J/E = JARDÍN / ESTACIONAMIENTO	FT = FRANJA TÉCNICA
VC = VÍA CICLISTA	FC = FRANJA DE CIRCULACIÓN
BC = BERMA CENTRAL	S = SEPARADOR CENTRAL O LATERAL
PP = PISTA PRINCIPAL	TP = PISTA EXCLUSIVA DE TRANSPORTE PÚBLICO COLECTIVO
PS = PISTA SECUNDARIA	



ANEXO 01 DEL REGLAMENTO DE GESTIÓN DE ESPACIOS PÚBLICOS: FRANJAS FUNCIONALES DEL SISTEMA VIAL DEL DISTRITO DE SAN BORJA

Descripción: SISTEMA VIAL DISTRITAL DE SAN BORJA

Vía: AVENIDA DE LA POESIA

Escala: 1/250


Distrito: SAN BORJA

Año: 2026

Lámina:


VLP-AV-06
(1 de 2)

ESPACIO DE ESTANCIA

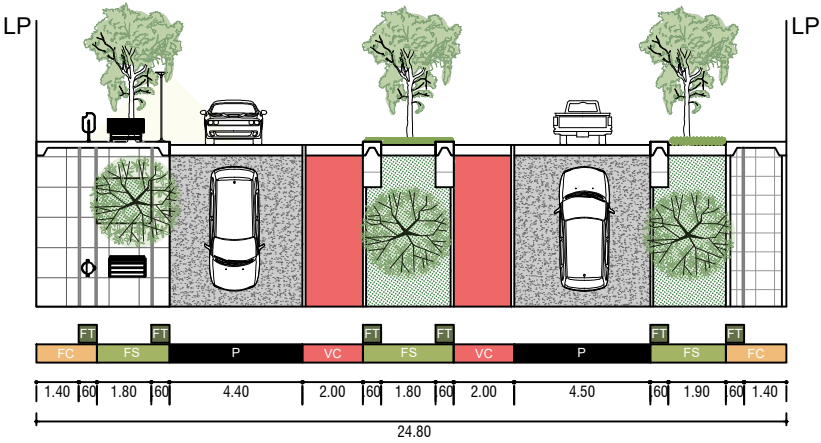

- 1. FS: Si la Franja de Servicio mide mayor o igual a 1.20 m, se debe implementar mobiliario complementario y de permanencia en zonas residenciales indicado en el Reglamento de Ornato y Mobiliario.
- 2. FS: Destinar parte de la Franja de Servicio a la colocación de arborización con alcorque indicado en el Reglamento de Ornato y Mobiliario.
- 3. FT: En la Franja Técnica se pueden colocar postes de telefonía, postes de luz, señalética vertical, tachos segregadores y elementos similares indicados en el Reglamento de Ornato y Mobiliario.
- 4. FC: Si la Franja de Circulación mide mayor o igual a 1.80 m, se debe incluir loseta podotáctil indicada en el Reglamento de Ornato y Mobiliario.

ESTACIONAMIENTO PÚBLICO

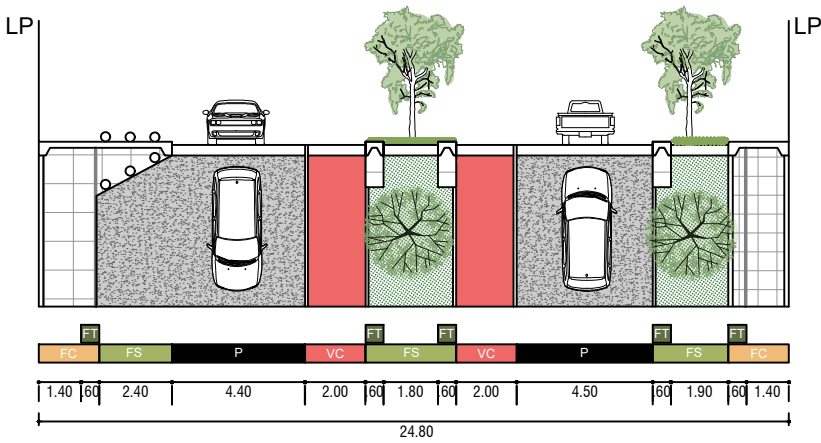

- 1. FS: Si es que no se cumple el ancho mínimo normativo para el estacionamiento del vehículo este no debe quedar expuesto en la pista PRINCIPAL (PP). De no existir zona rígida ni vegetación el ancho de la franja de servicio para estacionamiento será de 2.60m.
- 2. FS: Si la Franja de Servicio mide mayor o igual a 1.20 m, se debe implementar arborización indicada en el Reglamento de Ornato y Mobiliario.
- 3. FT: En la Franja Técnica de pueden colocar postes de telefonía, postes de luz, señalética vertical, tachos segregadores y elementos similares indicados en el Reglamento de Ornato y Mobiliario.
- 4. FC: Si la Franja de Circulación mide mayor o igual a 1.80 m, se debe incluir loseta podotáctil indicada en el Reglamento de Ornato y Mobiliario.

AVENIDA DE LA POESIA (24.80 m)

Sector: 1
Subsector: A
Tramo: Av. Javier Prado Este - Av. Canada

- NOTAS:**
- 1. Cualquier elemento que se instale en la Franja Técnica deberá formar parte del Núcleo Técnico Urbano, entendido como el sistema que organiza y agrupa los elementos autorizados dentro del espacio público, a fin de evitar instalaciones aisladas que comprometan la continuidad, la legibilidad y la seguridad del recorrido peatonal.

LEYENDA

- LP = LÍMITE DE PROPIEDAD
- V = VEREDA
- J/E = JARDÍN / ESTACIONAMIENTO
- VC = VÍA CICLISTA
- BC = BERMA CENTRAL
- PP = PISTA PRINCIPAL
- PS = PISTA SECUNDARIA
- FE = FRANJA EXCEPCIONAL
- FS = FRANJA DE SERVICIO
- FT = FRANJA TÉCNICA
- FC = FRANJA DE CIRCULACIÓN
- S = SEPARADOR CENTRAL O LATERAL
- TP = PISTA EXCLUSIVA DE TRANSPORTE PÚBLICO COLECTIVO