



ESPACIO PAISAJISTA

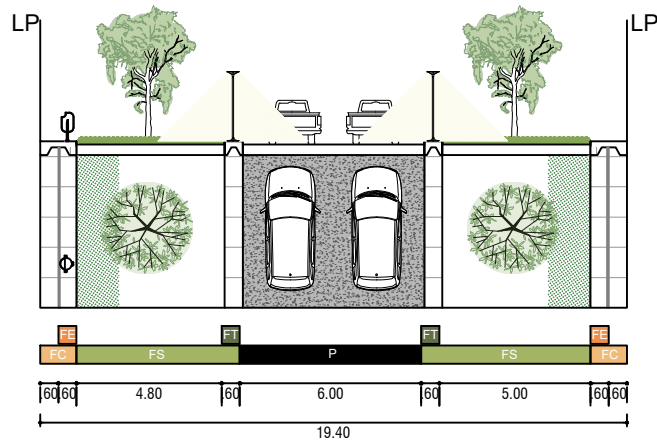

1. FS: Si la Franja de Servicio mide mayor o igual a 1.20m; se debe implementar arborización indicada en el Reglamento de Ornato y Mobiliario.
2. FT: En la Franja Técnica se pueden colocar postes de telefonía, postes de luz, señalética vertical, tachos segregadores y elementos similares indicados en el Reglamento de Ornato y Mobiliario.
3. FC: Si la Franja de Circulación mide mayor o igual a 1.80 m, se deberá incluir loseta podotáctil, de acuerdo con lo indicado en el Reglamento de Ornato y Mobiliario.

ESPACIO DE ESTANCIA

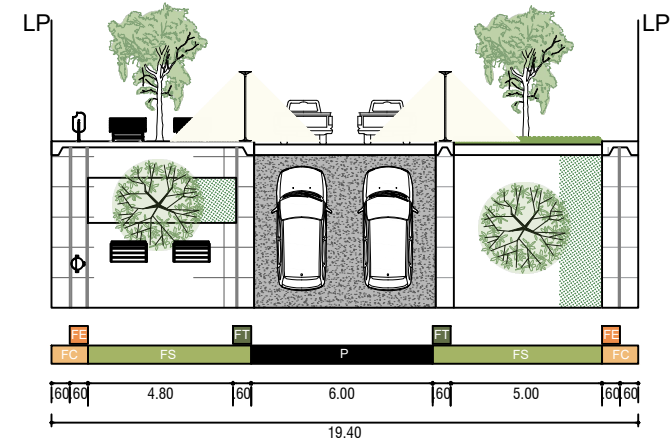

1. FS: Si la Franja de Servicio mide mayor o igual a 1.20m; se debe implementar mobiliario complementario y de permanencia en zonas residenciales indicado en el Reglamento de Ornato y Mobiliario.
2. FS: Destinar parte de la Franja de Servicio a la colocación de arborización con alcorque indicado en el Reglamento de Ornato y Mobiliario.
3. FT: En la Franja Técnica se pueden colocar postes de telefonía, postes de luz, señalética vertical, tachos segregadores y elementos similares indicados en el Reglamento de Ornato y Mobiliario.
4. FC: Si la Franja de Circulación mide mayor o igual a 1.80 m, se deberá incluir loseta podotáctil, de acuerdo con lo indicado en el Reglamento de Ornato y Mobiliario.

CALLE JORGE MUELLE (19.40 m)

Sector: 10

Subsector: B

Tramo: Calle Jorge Muelle (tramo D) - Calle Jorge Muelle (tramo B)

NOTAS:

1. Cualquier elemento que se instale en la Franja Técnica deberá formar parte del Núcleo Técnico Urbano, entendido como el sistema que organiza y agrupa los elementos autorizados dentro del espacio público, a fin de evitar instalaciones aisladas que comprometan la continuidad, la legibilidad y la seguridad del recorrido peatonal.

LEYENDA

LP = LÍMITE DE PROPIEDAD

V = VEREDA

J/E = JARDÍN / ESTACIONAMIENTO

VC = VÍA CICLISTA

BC = BERMA CENTRAL

PP = PISTA PRINCIPAL

PS = PISTA SECUNDARIA

FE = FRANJA EXCEPCIONAL

FS = FRANJA DE SERVICIO

FT = FRANJA TÉCNICA

FC = FRANJA DE CIRCULACIÓN

S = SEPARADOR CENTRAL O LATERAL

TP = PISTA EXCLUSIVA DE TRANSPORTE PÚBLICO COLECTIVO



ANEXO 01 DEL REGLAMENTO DE GESTIÓN DE ESPACIOS PÚBLICOS: FRANJAS FUNCIONALES DEL SISTEMA VIAL DEL DISTRITO DE SAN BORJA

Descripción: SISTEMA VIAL DISTRITAL DE SAN BORJA

Vía: CALLE JORGE MUELLE

Escala: 1/250


Districto: SAN BORJA

Año: 2026

Lámina:


VLP-CA-36C
(1 de 2)

EXTENSIÓN DE COMERCIO

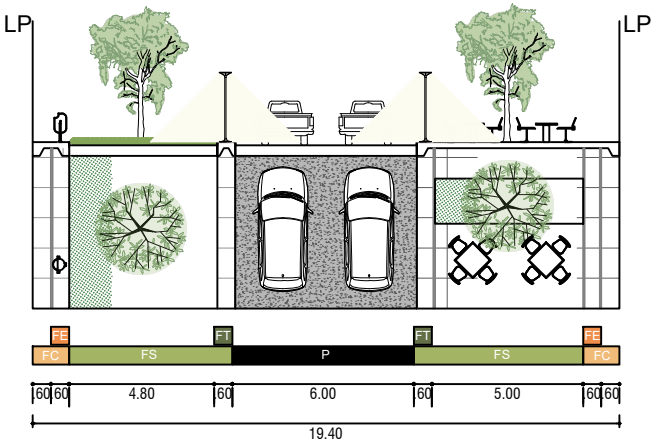

- 1. FC: Si la Franja de Circulación fuera colindante a un predio con licencia de funcionamiento se habilitará una extensión en la Franja de Servicio si es mayor o igual a 1.80m., donde se debe implementar mobiliario que genere espacios de extensión para los comercios indicado en el Reglamento de Ornato y Mobiliario.
- 2. FT: En la Franja Técnica de pueden colocar postes de telefonía, postes de luz, señalética vertical, tachos segregadores y elementos similares indicados en el Reglamento de Ornato y Mobiliario.
- 3. FC: Si la Franja de Circulación mide mayor o igual a 1.80 m, se deberá incluir loseta podotáctil, de acuerdo con lo indicado en el Reglamento de Ornato y Mobiliario.

ESTACIONAMIENTO PÚBLICO

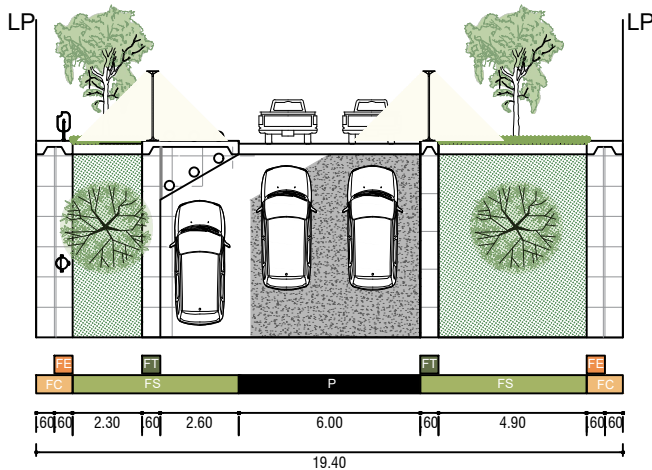

- 1. FS: Si es que no se cumple el ancho mínimo normativo para el estacionamiento del vehículo este no debe quedar expuesto en la pista PRINCIPAL (PP). De no existir zona rígida ni vegetación el ancho de la franja de servicio para estacionamiento será de 2.60m.
- 2. FS: Si la Franja de Servicio mide mayor o igual a 1.20m; se debe implementar arborización indicada en el Reglamento de Ornato y Mobiliario.
- 3. FT: En la Franja Técnica de pueden colocar postes de telefonía, postes de luz, señalética vertical, tachos segregadores y elementos similares indicados en el Reglamento de Ornato y Mobiliario.
- 4. FC: Si la Franja de Circulación mide mayor o igual a 1.80m; se debe incluir loseta podotáctil indicada en el Reglamento de Ornato y Mobiliario.

CALLE JORGE MUELLE (19.40 m)

Sector: 10

Subsector: B

Tramo: Calle Jorge Muelle (tramo D) - Calle Jorge Muelle (tramo B)

NOTAS:

- 1. Cualquier elemento que se instale en la Franja Técnica deberá formar parte del Núcleo Técnico Urbano, entendido como el sistema que organiza y agrupa los elementos autorizados dentro del espacio público, a fin de evitar instalaciones aisladas que comprometan la continuidad, la legibilidad y la seguridad del recorrido peatonal.

LEYENDA

- | | |
|--------------------------------|--|
| LP = LÍMITE DE PROPIEDAD | FE = FRANJA EXCEPCIONAL |
| V = VEREDA | FS = FRANJA DE SERVICIO |
| J/E = JARDÍN / ESTACIONAMIENTO | FT = FRANJA TÉCNICA |
| VC = VÍA CICLISTA | FC = FRANJA DE CIRCULACIÓN |
| BC = BERMA CENTRAL | S = SEPARADOR CENTRAL O LATERAL |
| PP = PISTA PRINCIPAL | TP = PISTA EXCLUSIVA DE TRANSPORTE PÚBLICO COLECTIVO |
| PS = PISTA SECUNDARIA | |



ANEXO 01 DEL REGLAMENTO DE GESTIÓN DE ESPACIOS PÚBLICOS: FRANJAS FUNCIONALES DEL SISTEMA VIAL DEL DISTRITO DE SAN BORJA

Descripción: SISTEMA VIAL DISTRITAL DE SAN BORJA

Vía: CALLE JORGE MUELLE

Escala: 1/250

Districto: SAN BORJA

Año: 2026

Lámina:

VLP-CA-36C
(2 de 2)