


ESPACIO PAISAJISTA

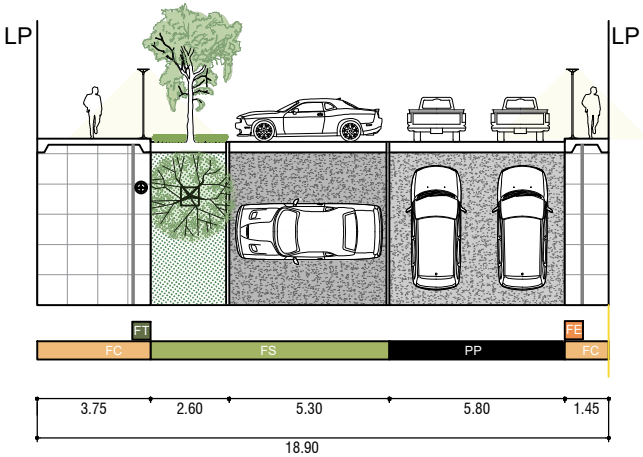

1. FS: Si la Franja de Servicio mide mayor o igual a 1.20 m, se debe implementar arborización indicada en el Reglamento de Ornato y Mobiliario.
2. FT: En la Franja Técnica se pueden colocar postes de telefonía, postes de luz, señalética vertical, tachos segregadores y elementos similares indicados en el Reglamento de Ornato y Mobiliario.
3. FC: Si la Franja de Circulación mide mayor o igual a 1.80 m, se deberá incluir loseta podotáctil, de acuerdo con lo indicado en el Reglamento de Ornato y Mobiliario.

PASAJE EDUARDO YOUNG BAZO (18.90 m)

Sector: 10
Subsector: C
Tramo: Ca. Eduardo Orrego Villacorta - Psj. Miguel Baca Rossi

- NOTAS:**
1. Cualquier elemento que se instale en la Franja Técnica deberá formar parte del Núcleo Técnico Urbano, entendido como el sistema que organiza y agrupa los elementos autorizados dentro del espacio público, a fin de evitar instalaciones aisladas que comprometan la continuidad, la legibilidad y la seguridad del recorrido peatonal.

LEYENDA

- | | |
|--------------------------------|--|
| LP = LÍMITE DE PROPIEDAD | FE = FRANJA EXCEPCIONAL |
| V = VEREDA | FS = FRANJA DE SERVICIO |
| J/E = JARDÍN / ESTACIONAMIENTO | FT = FRANJA TÉCNICA |
| VC = VÍA CICLISTA | FC = FRANJA DE CIRCULACIÓN |
| BC = BERMA CENTRAL | S = SEPARADOR CENTRAL O LATERAL |
| PP = PISTA PRINCIPAL | TP = PISTA EXCLUSIVA DE TRANSPORTE PÚBLICO COLECTIVO |
| PS = PISTA SECUNDARIA | |

Descripción: SISTEMA VIAL DISTRITAL DE SAN BORJA

Vía: PASAJE EDUARDO YOUNG BAZO

Escala: 1/250

Distrito: SAN BORJA

Año: 2026

Lámina:

VLS-PA-70C